


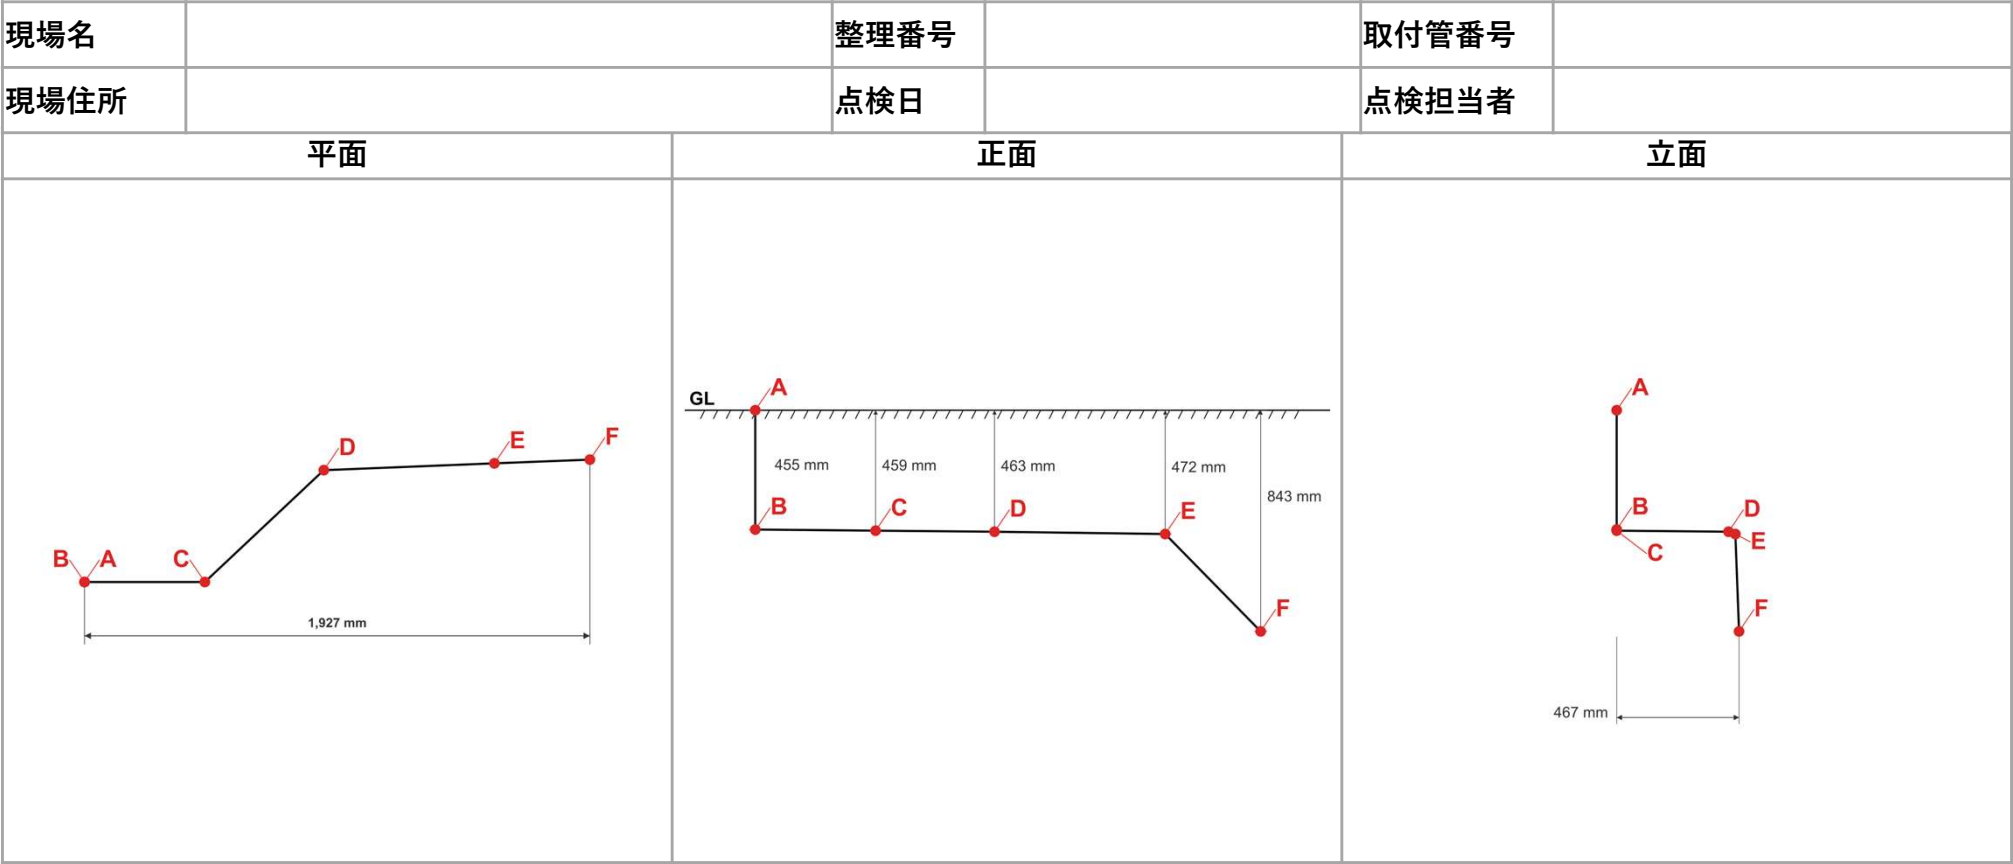


マッピング解析結果

区間	配管長 (mm)	角度 (合成角)	角度(°)	改築部材 No.
A→B	455	-	-	1
B→C	459	∠B	90.5	3
C→D	623	∠C	43.2	5
D→E	651	∠D	40.9	7
E→F	520	∠E	44.8	9

調査結果（特記事項）

No.	特記事項

※本面図は公共マス流出方向を基準として作成しております。
※角度は上流側から見た下流点への変化量を示しています（合成角）。

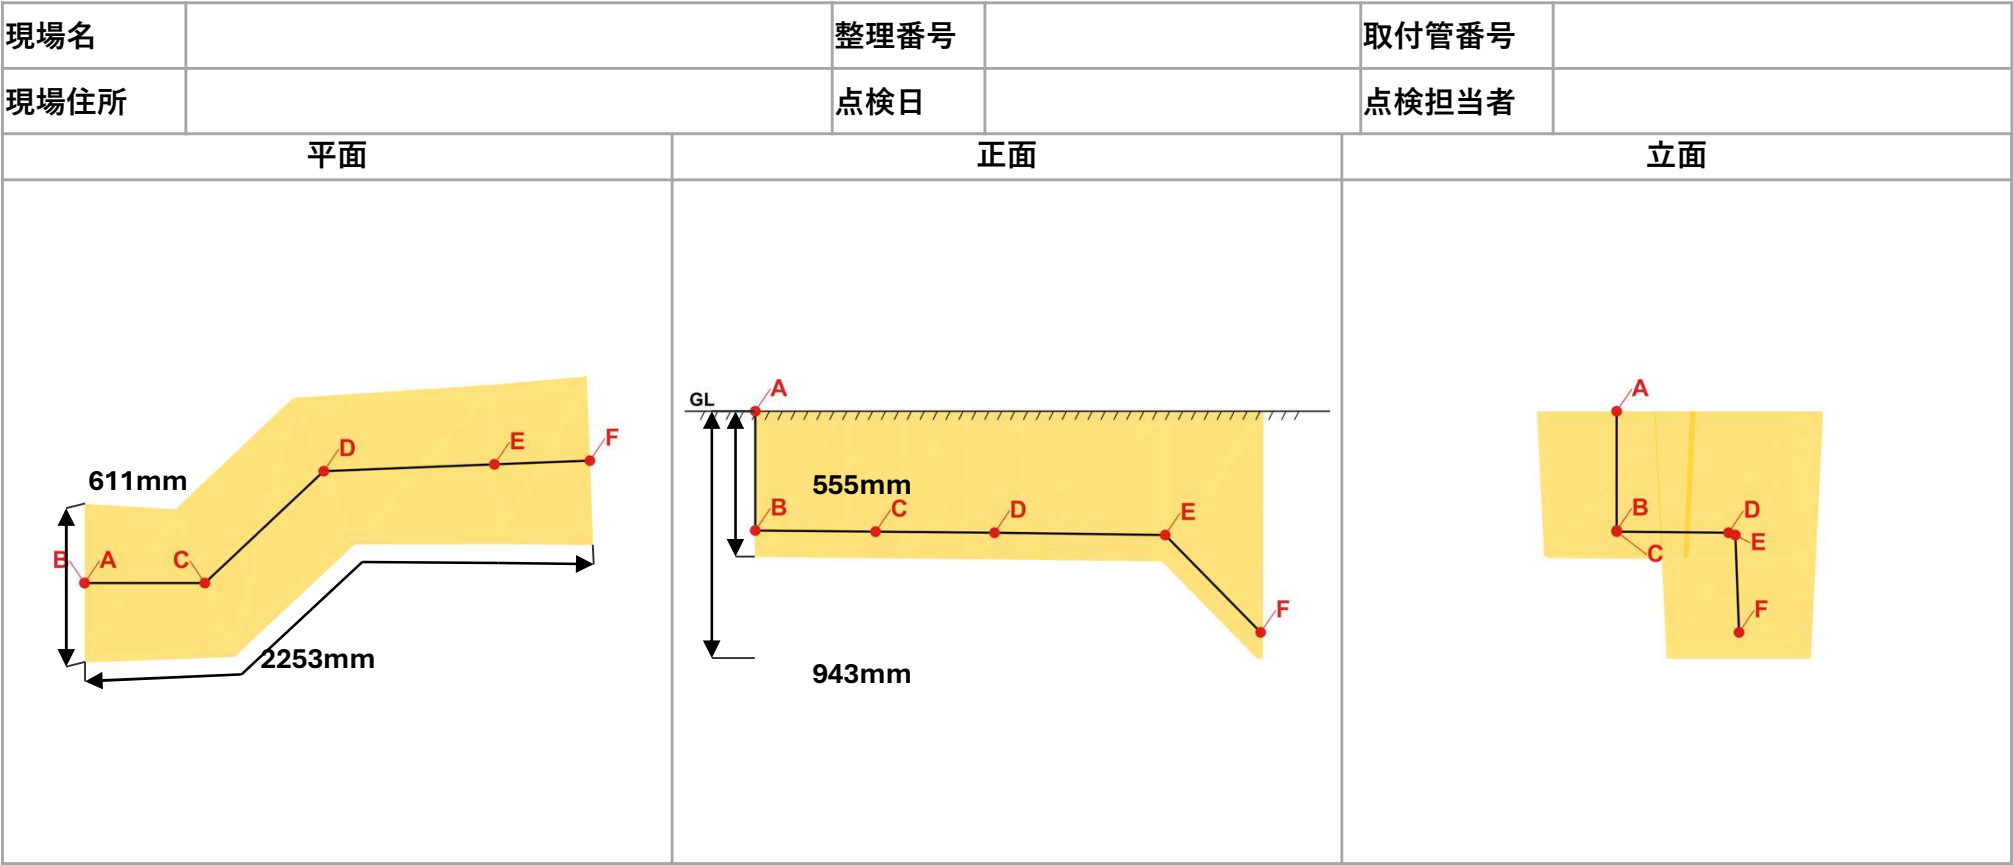

改築部材				土工量			
種目	略号・サイズ	数量	改築部材No.	種目	形状寸法	単位	数量
直管	立管 455mm	1	1	管路掘削		m ³	0.838
最終ます	MK 150P-200x0.6	1	2	管路埋戻		m ³	0.666
取付管	SRB 150x0.8m	1	3	発生土処理		m ³	0.172
曲管	30SR-F 150	1	4				
取付管	SRB 150x0.8m	1	5				
曲管	30SR-F 150	1	6				
取付管	SRB 150x0.8m	1	7				
曲管	30SR-F 150	1	8				
取付管	SRB 150x0.8m	1	9				
支管	90SHR 200-150	1	10				